


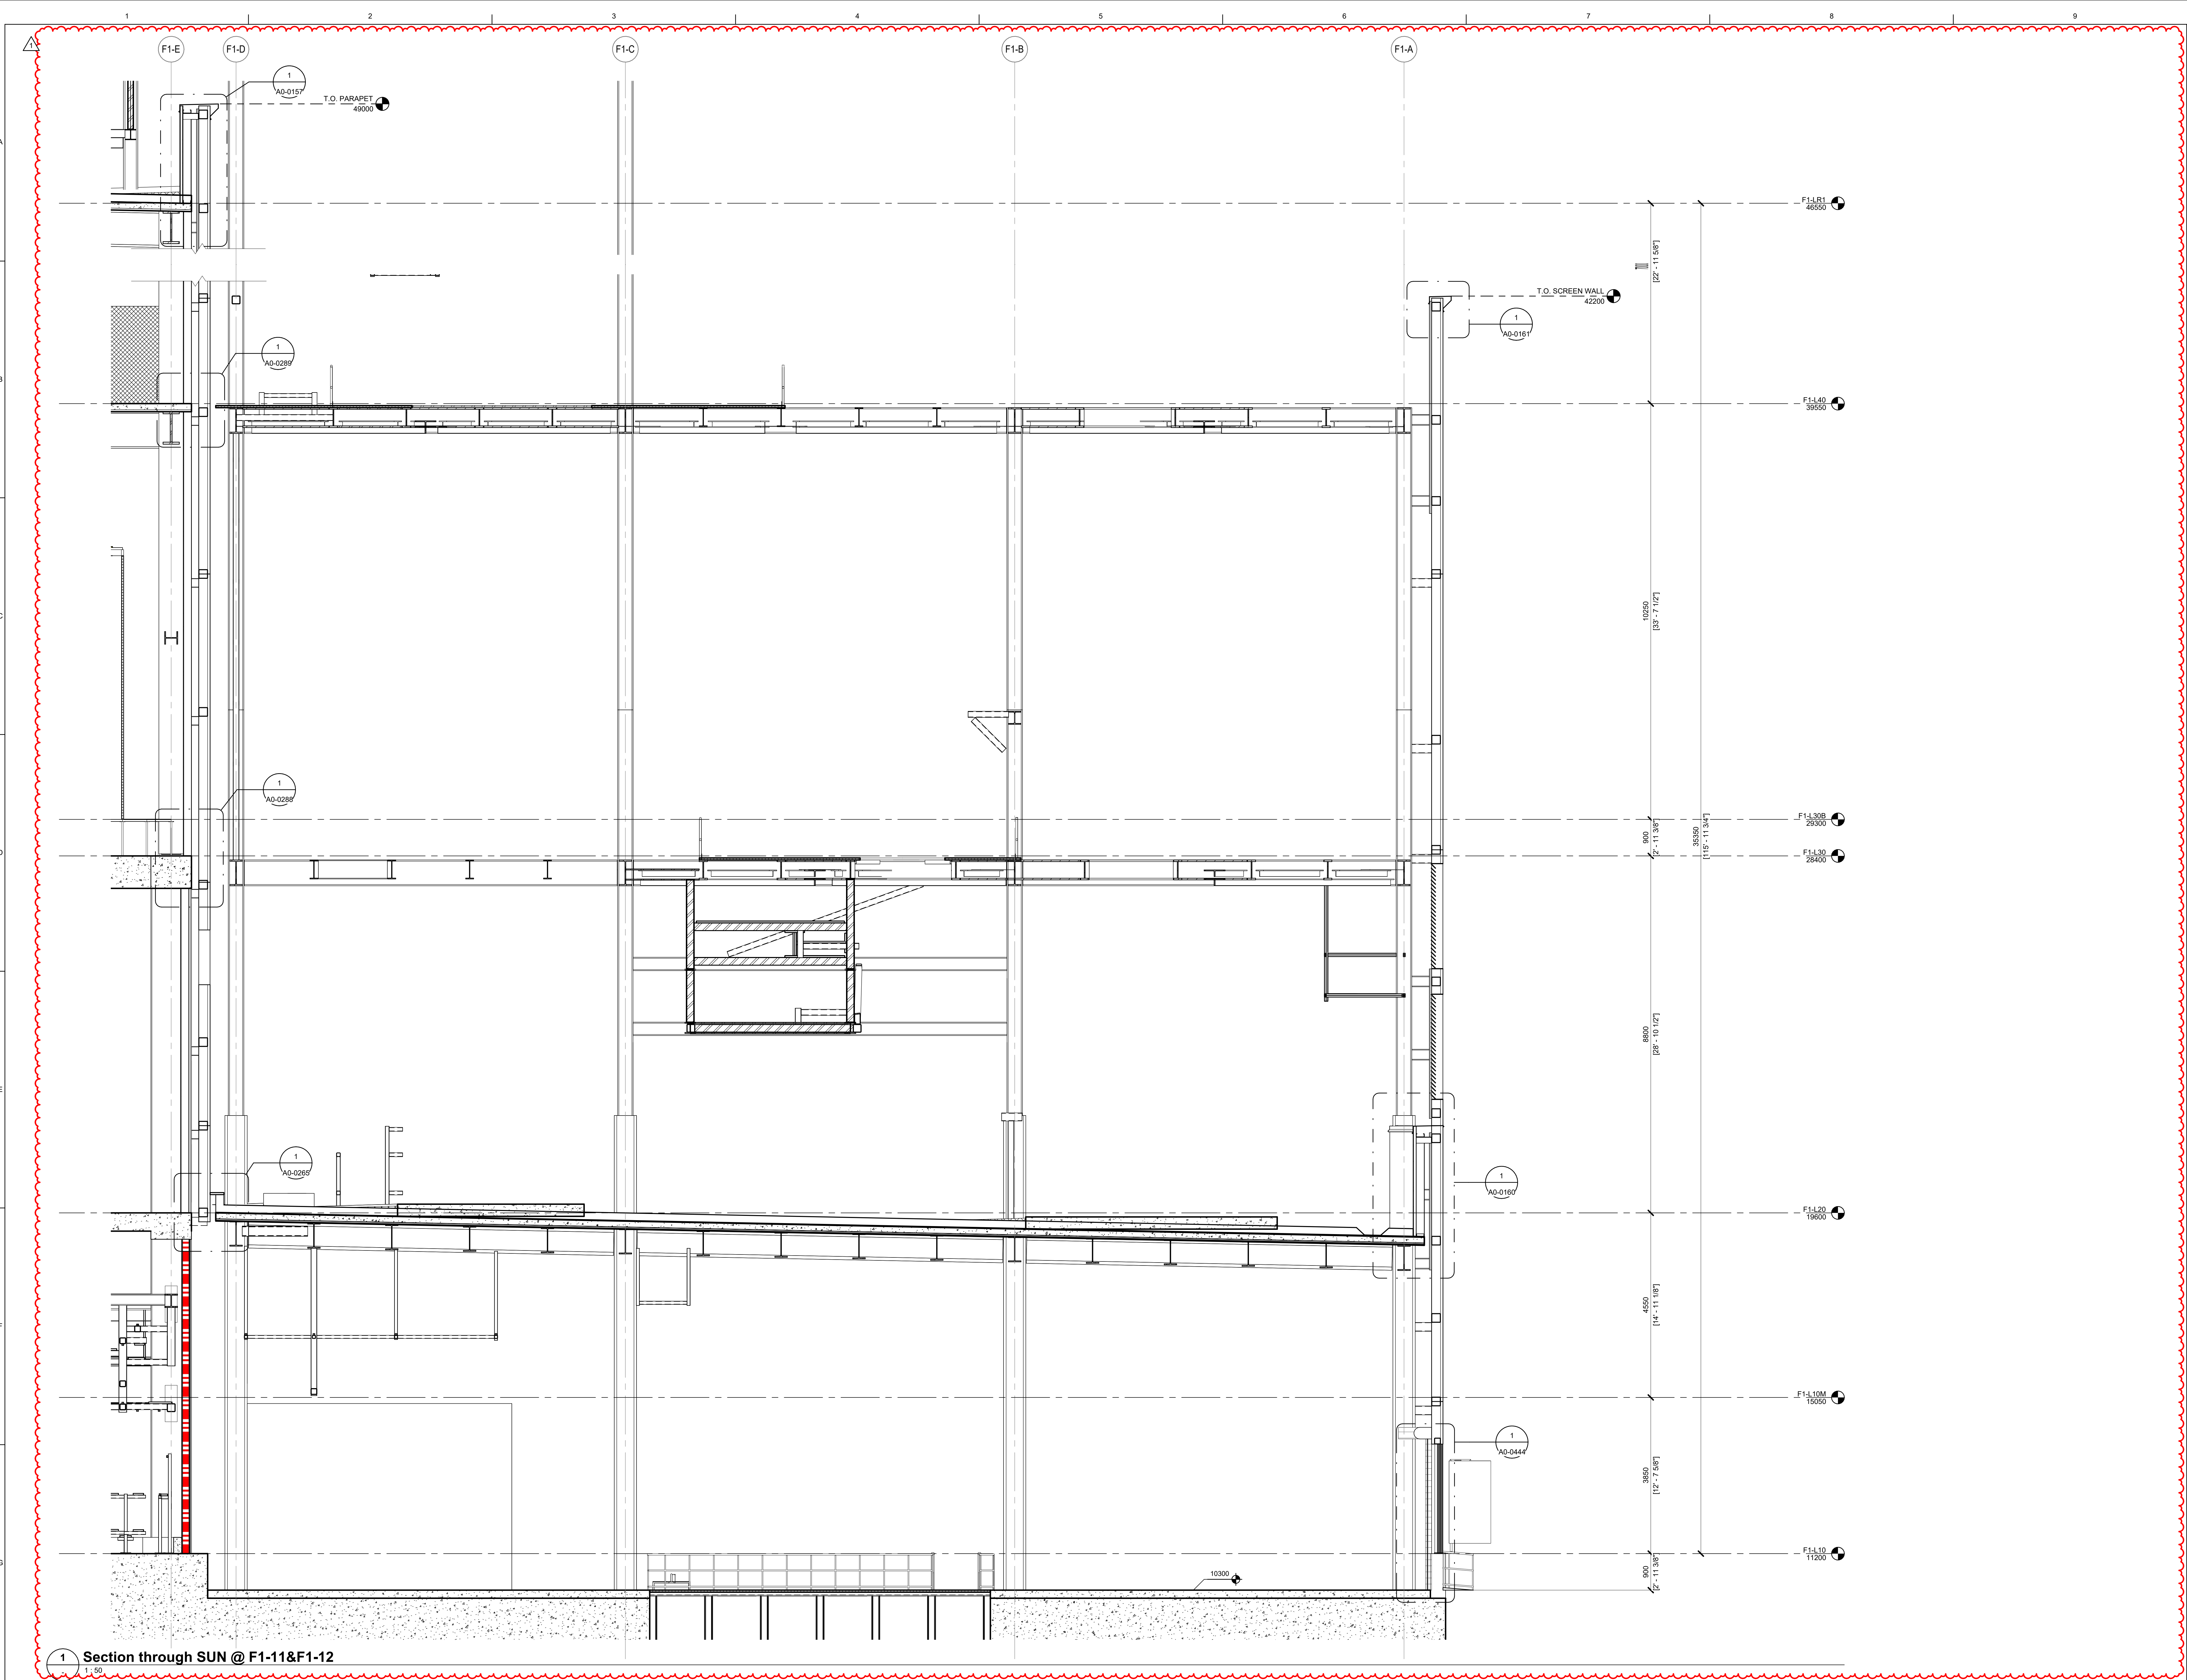


PRELIMINARY
- NOT FOR
CONSTRUCTION

REVISION				APPROVED	
NO.	DATE	ENGINEER	DESIGN	CHECK	SD
0	26/06/25	FR-0281	ISSUED FOR CONSTRUCTION	REVISION	VM



Project Title: DF1 DHOLERA SITE PHASE 1	
Drawing Title: FAB BUILDING 1 ARCHITECTURAL WALL SECTIONS	
Date:	26/06/2025
Scale:	1:50
Proj. No.:	03898800
Drawing No.:	FB1A0-7300

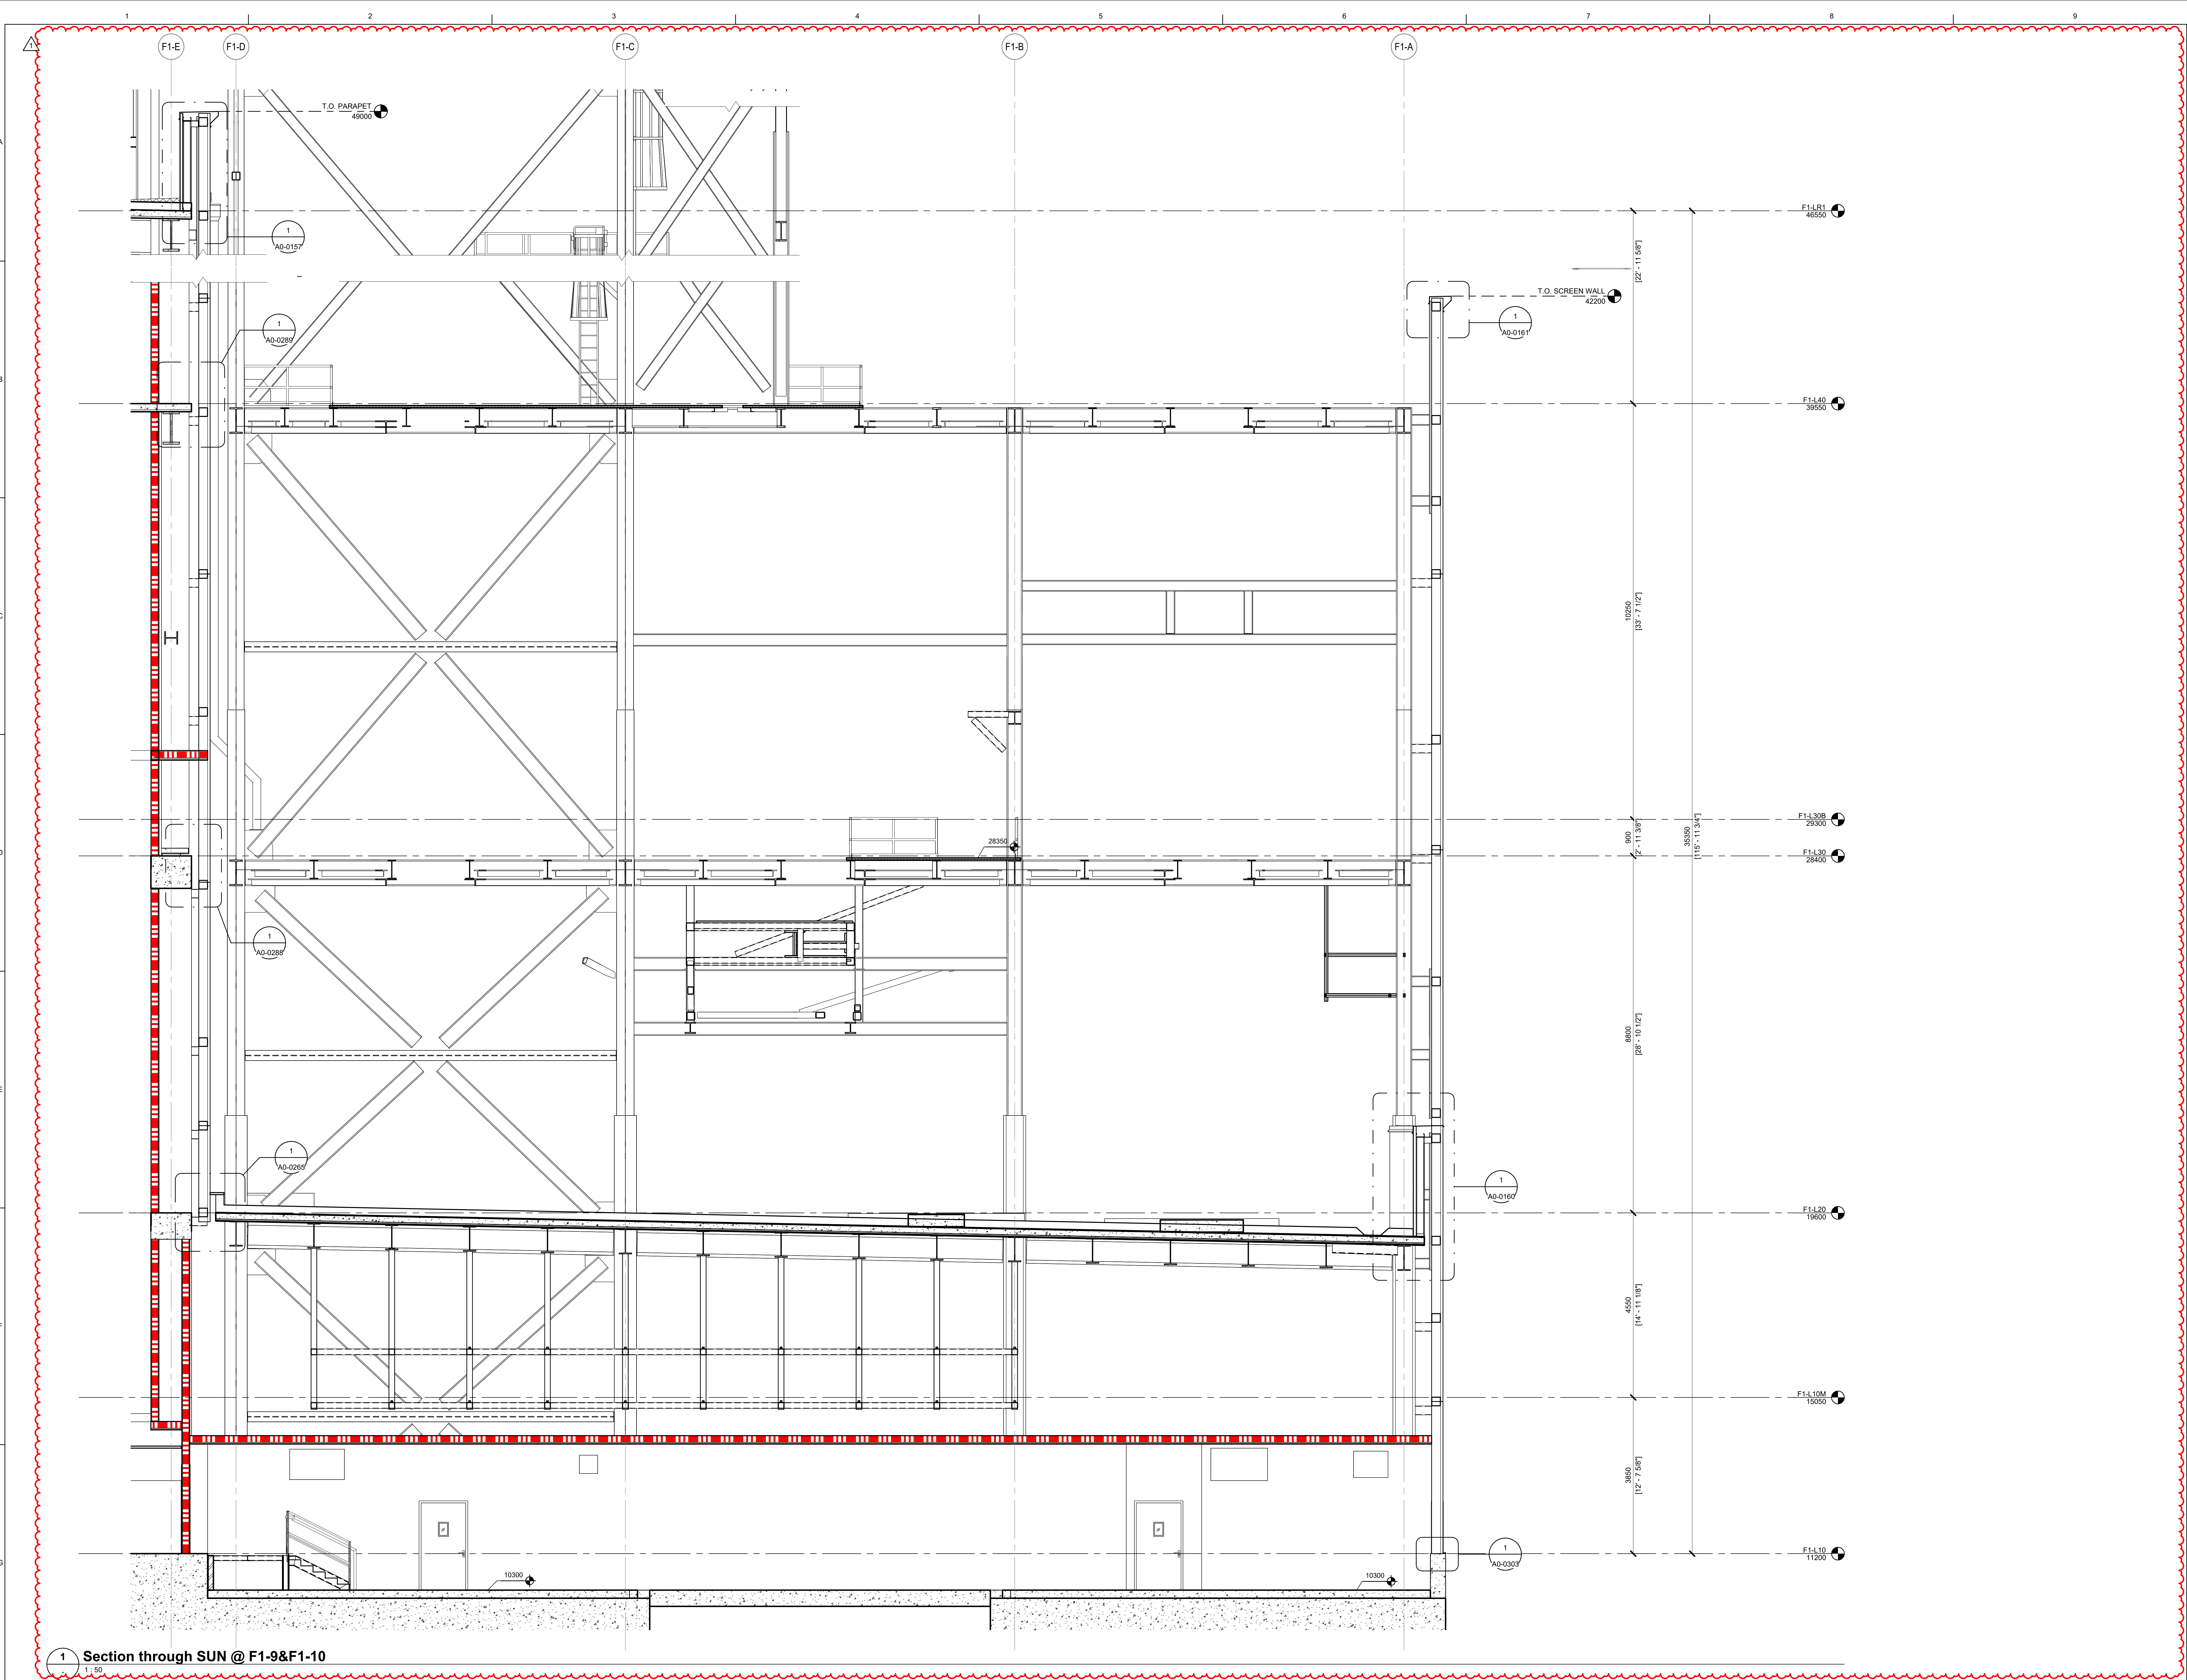


PRELIMINARY
- NOT FOR
CONSTRUCTION

REVISION				APPROVED			
NO.	DATE	ENGINEER	NO.	DATE	ENGINEER	NO.	DATE
0	26/06/25	FR-0281	0	26/06/25	FR-0281	0	26/06/25
ISSUED FOR CONSTRUCTION				ISSUED FOR CONSTRUCTION			
DRAWN				CHECK			
SD				IS			
DS				VM			




Project Title: **DF1 DHOLERA SITE PHASE 1**
Drawing Title: **FAB BUILDING 1 ARCHITECTURAL WALL SECTIONS**
Date: 26/06/2025
Scale: 1=50
Proj. No.: 03898800
Drawing No.: **FB1A0-7301**

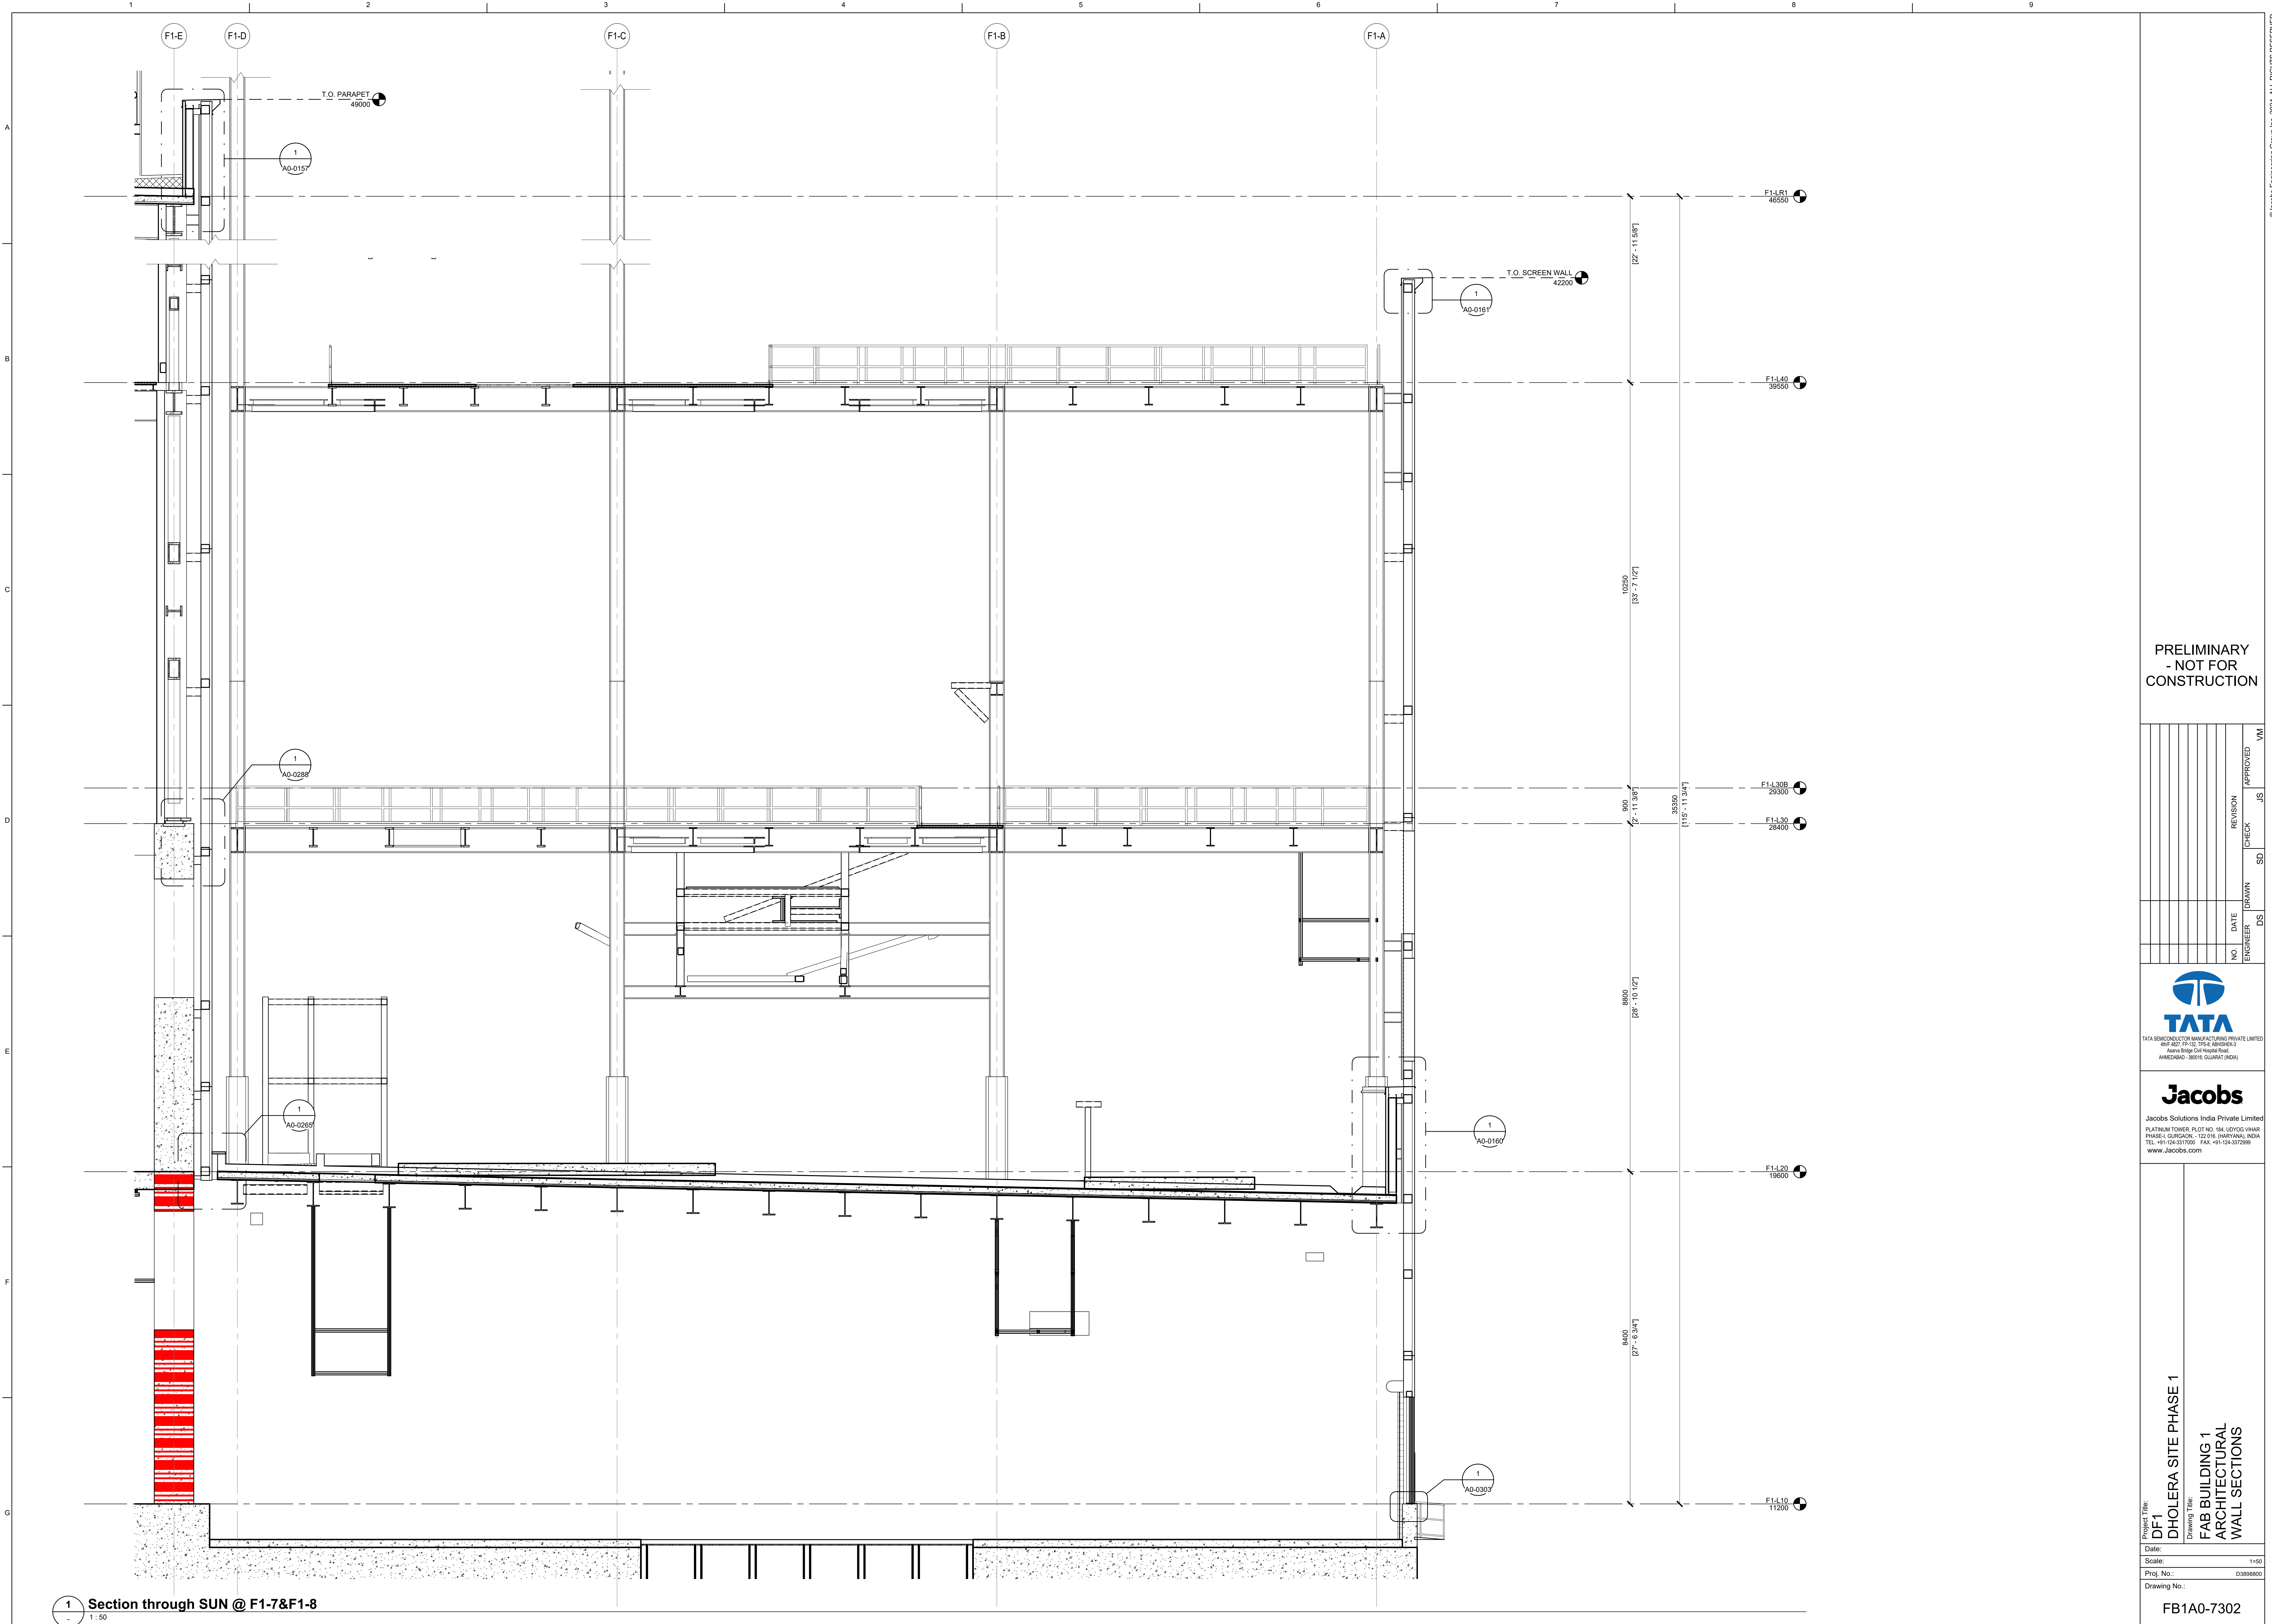

PRELIMINARY
- NOT FOR
CONSTRUCTION

NO.	ENGINEER	DATE	REVISION	CHECK	DRAWN	SD	IS	APPROVED	VM


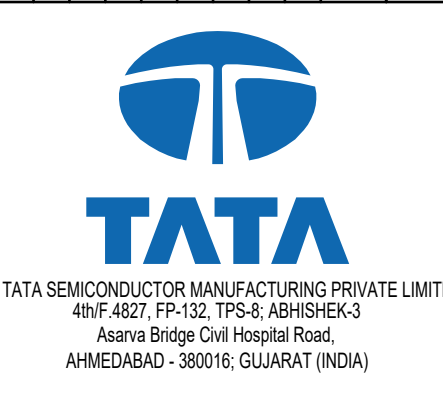


Project Title: DF1 DHOLERA SITE PHASE 1	
Drawing Title: FAB BUILDING 1 ARCHITECTURAL WALL SECTIONS	
Date:	11/05/2024
Scale:	1:50
Proj. No.:	03898800
Drawing No.:	FB1A0-7302



Jacobs
Jacobs Solutions India Private Limited
PLATINUM TOWER, PLOT NO. 184, UDYOG VIHAR
PHASE-I, GURGAON - 122 016, (HARYANA), INDIA
TEL. +91-124-3317000 FAX. +91-124-3372999
www.Jacobs.com

Project Title: DF1 Drawing Title: FAB BUILDING 1 ARCHITECTURAL WALL SECTIONS	
Date: 26/06/2023	Scale: 1=50
Proj. No.: D3886800	
Drawing No.: EB1A0-7303	

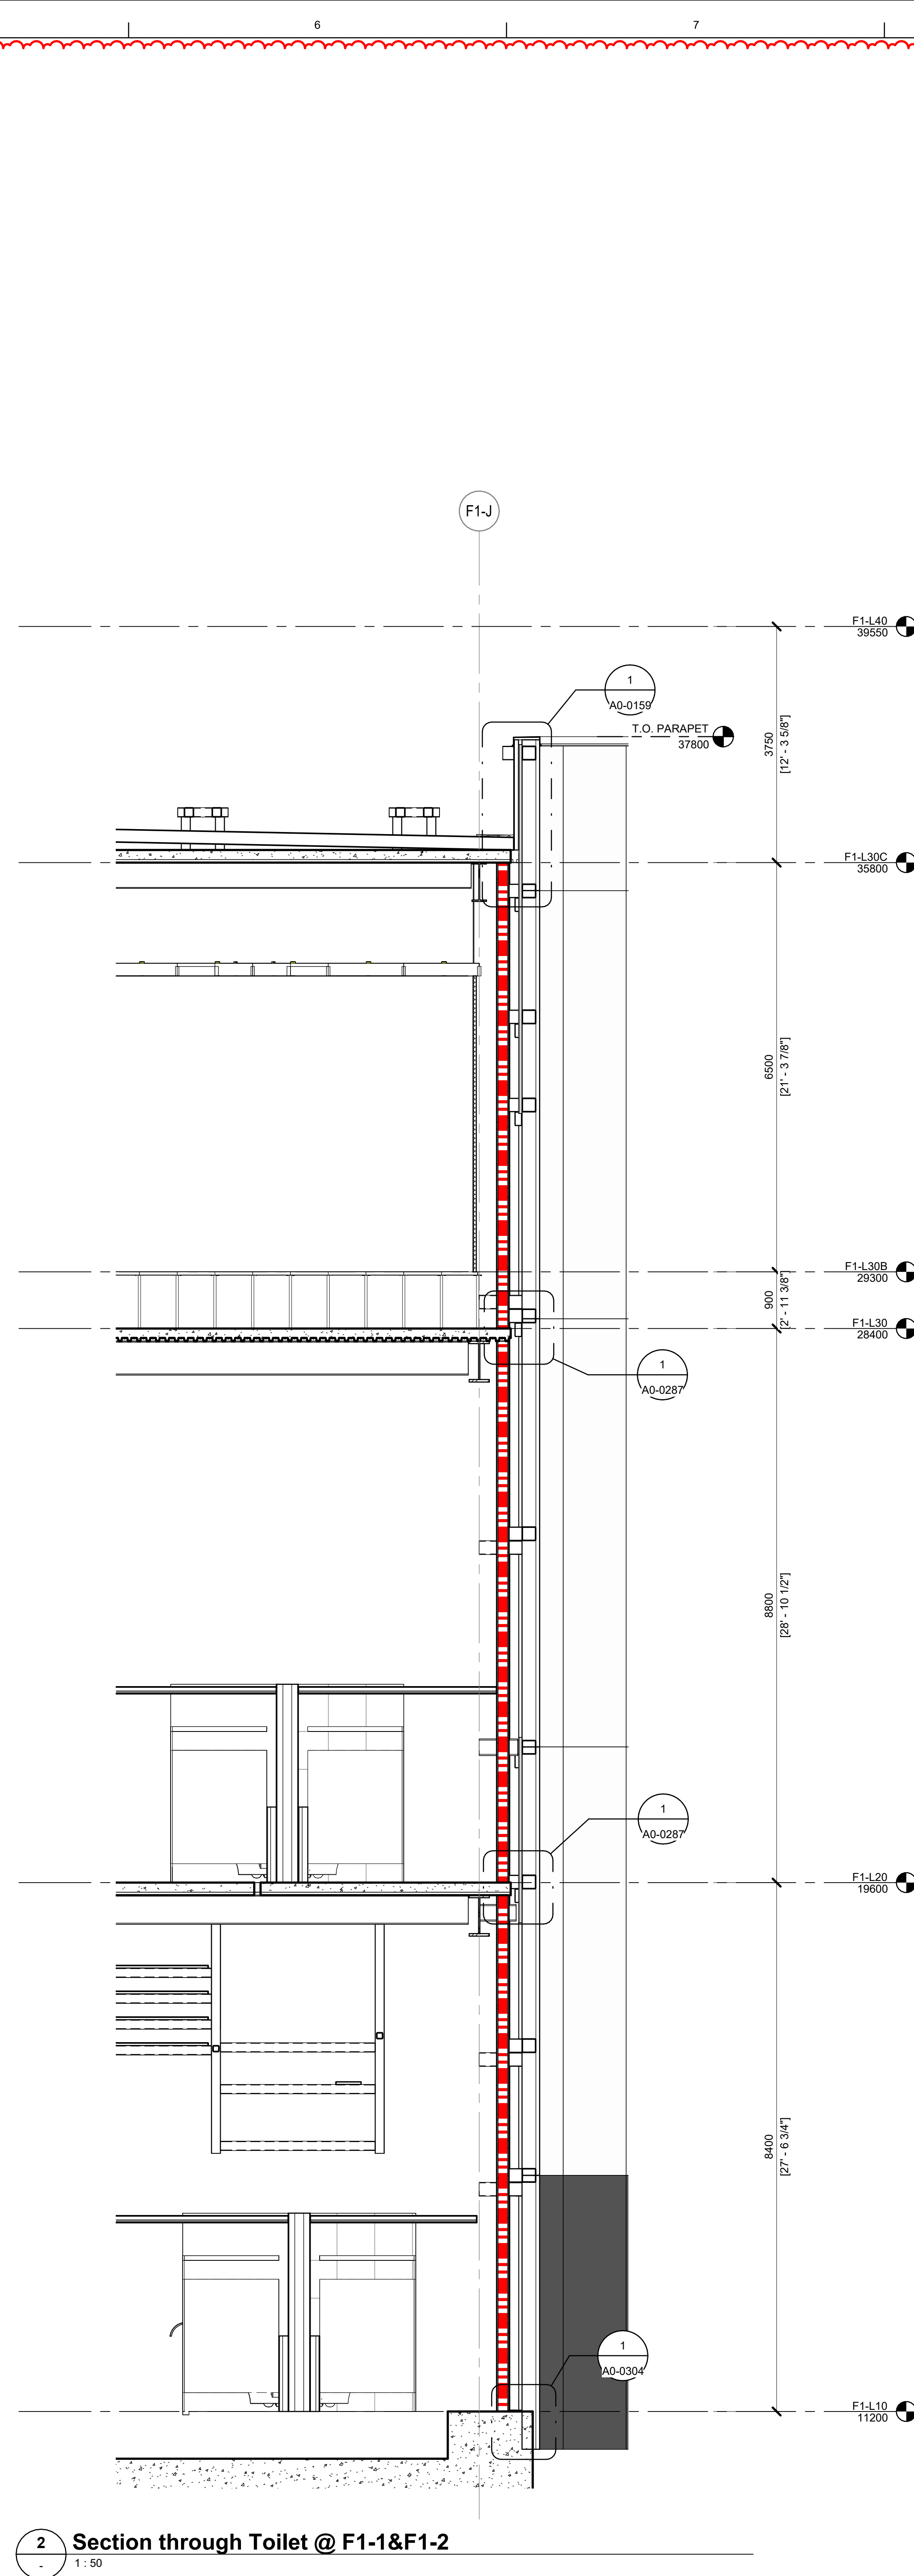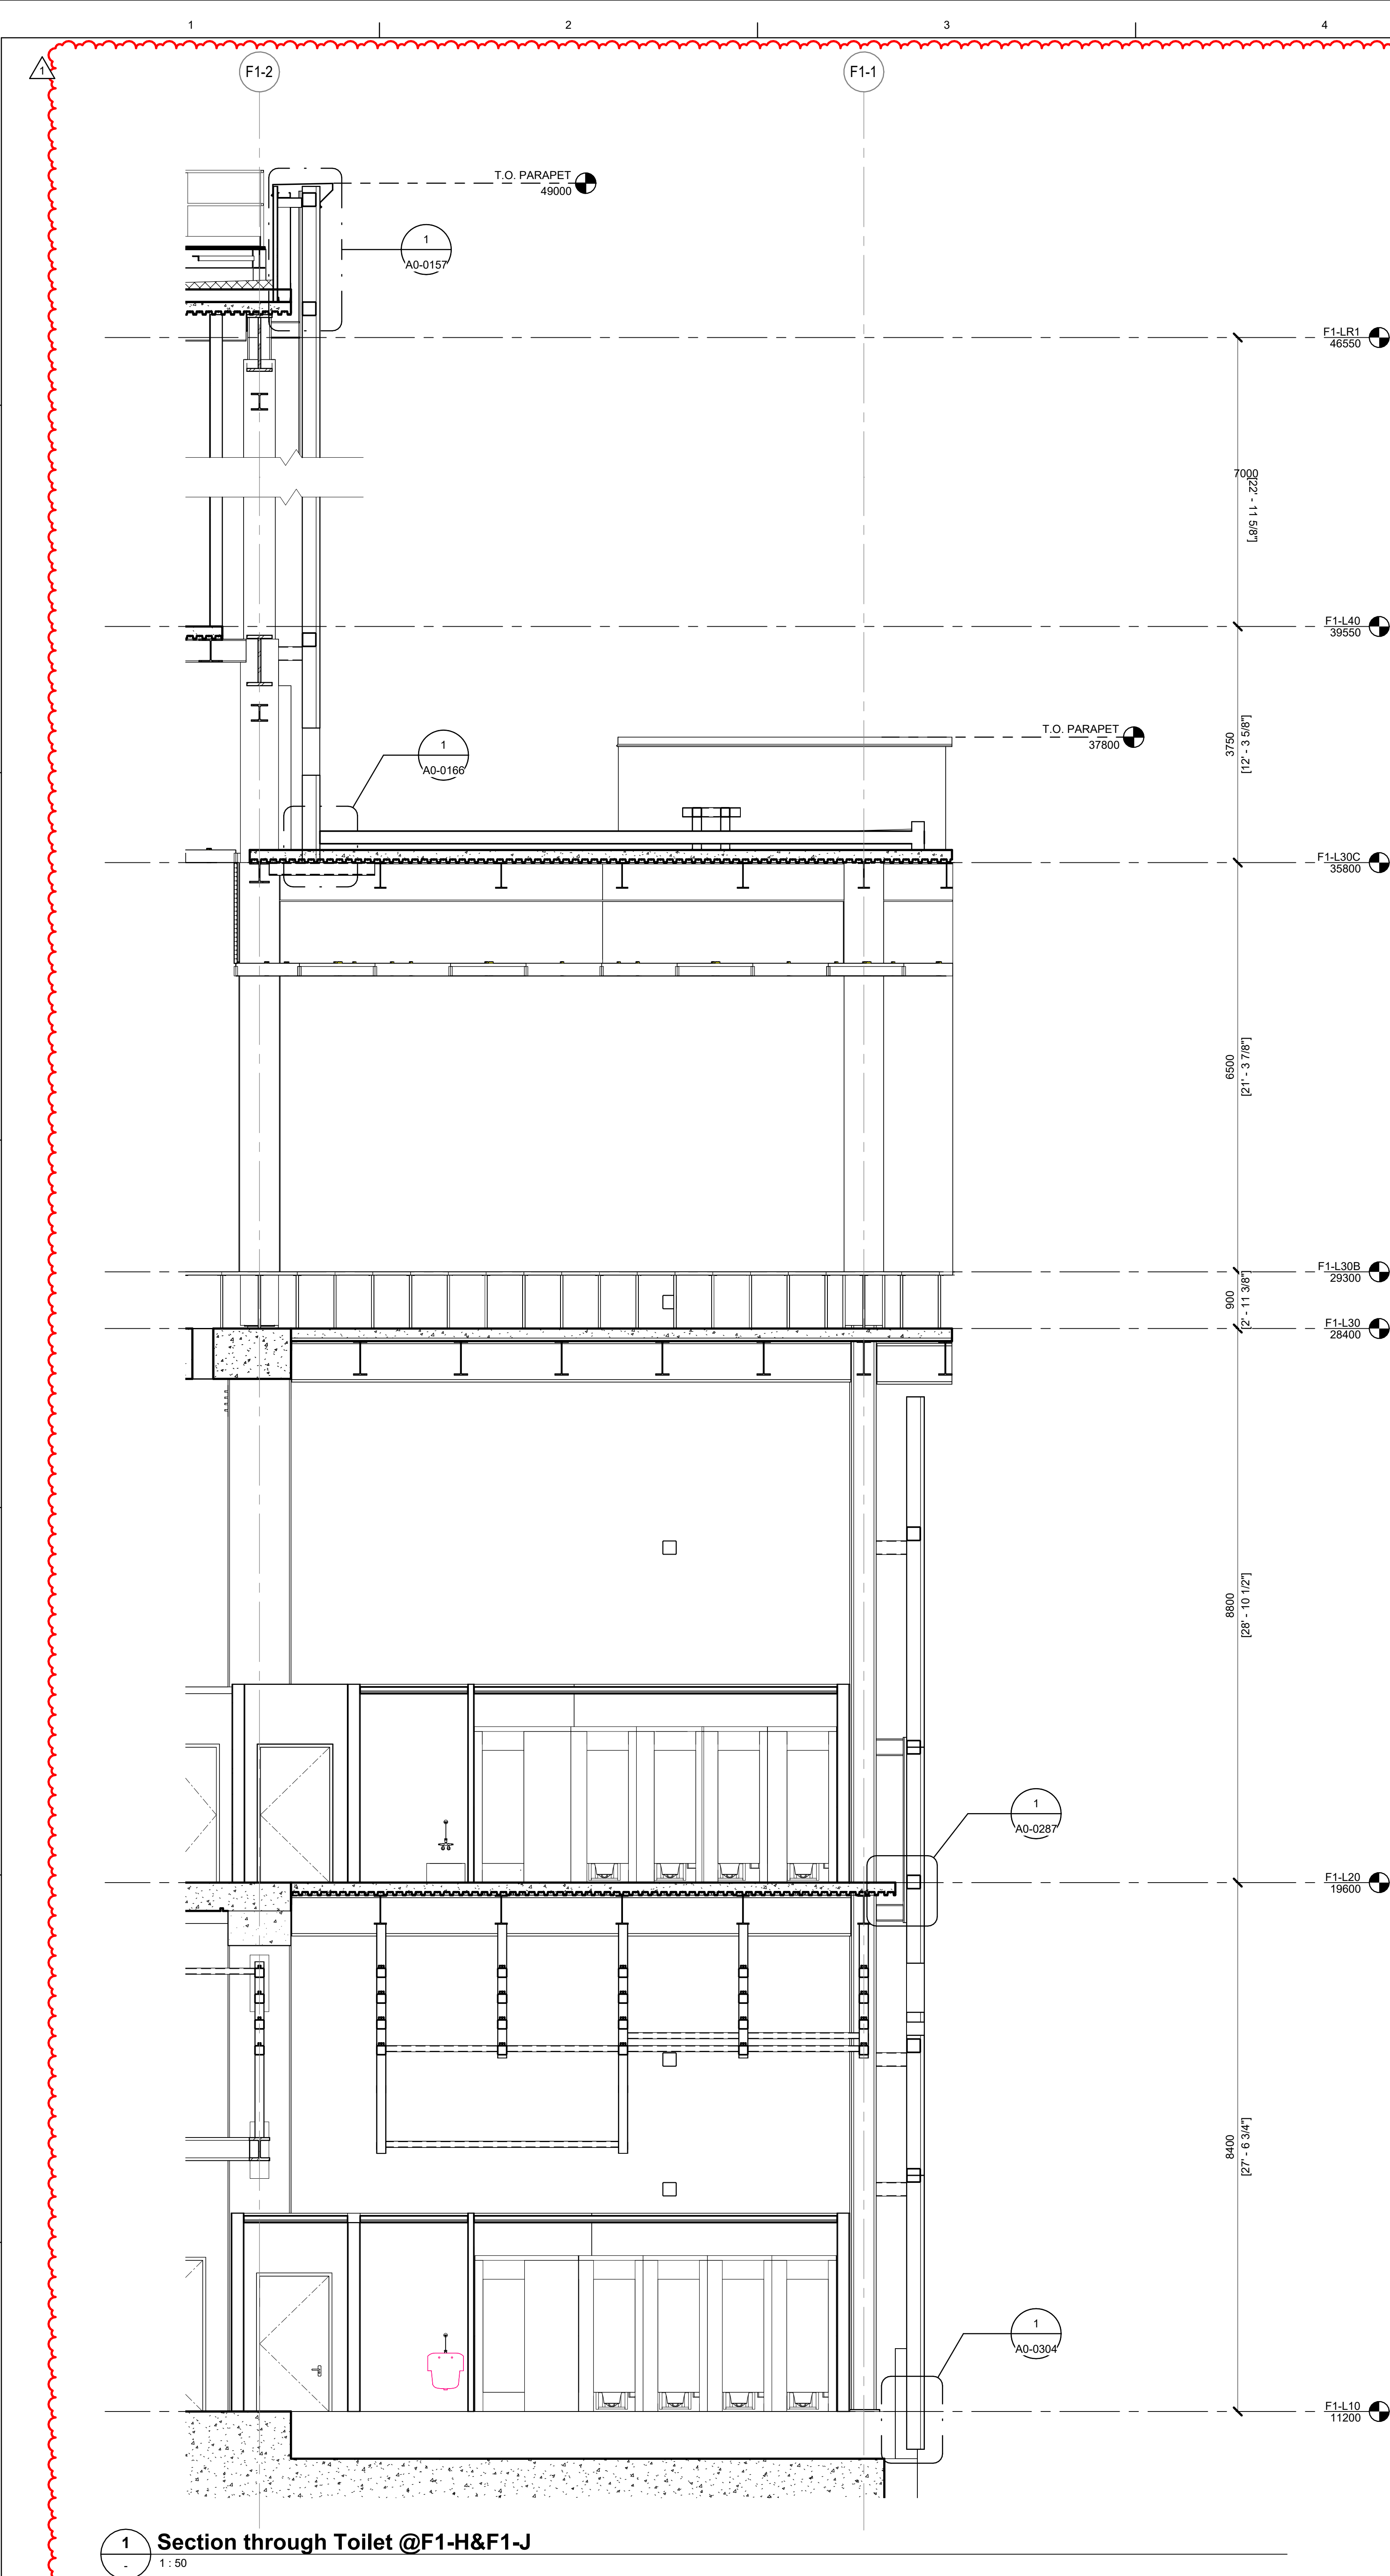


PRELIMINARY
- NOT FOR
CONSTRUCTION

NO.	DATE	REVISION	CHECK	APPROVED
0	26/06/2025	FR-0281 ISSUE FOR CONSTRUCTION	DS	VM



Project Title:	DF1 DHOLERA SITE PHASE 1
Drawing Title:	FAB BUILDING 1 ARCHITECTURAL WALL SECTIONS
Date:	25/06/2025
Scale:	1=50
Proj. No.:	03968800
Drawing No.:	

FB1A0-7304

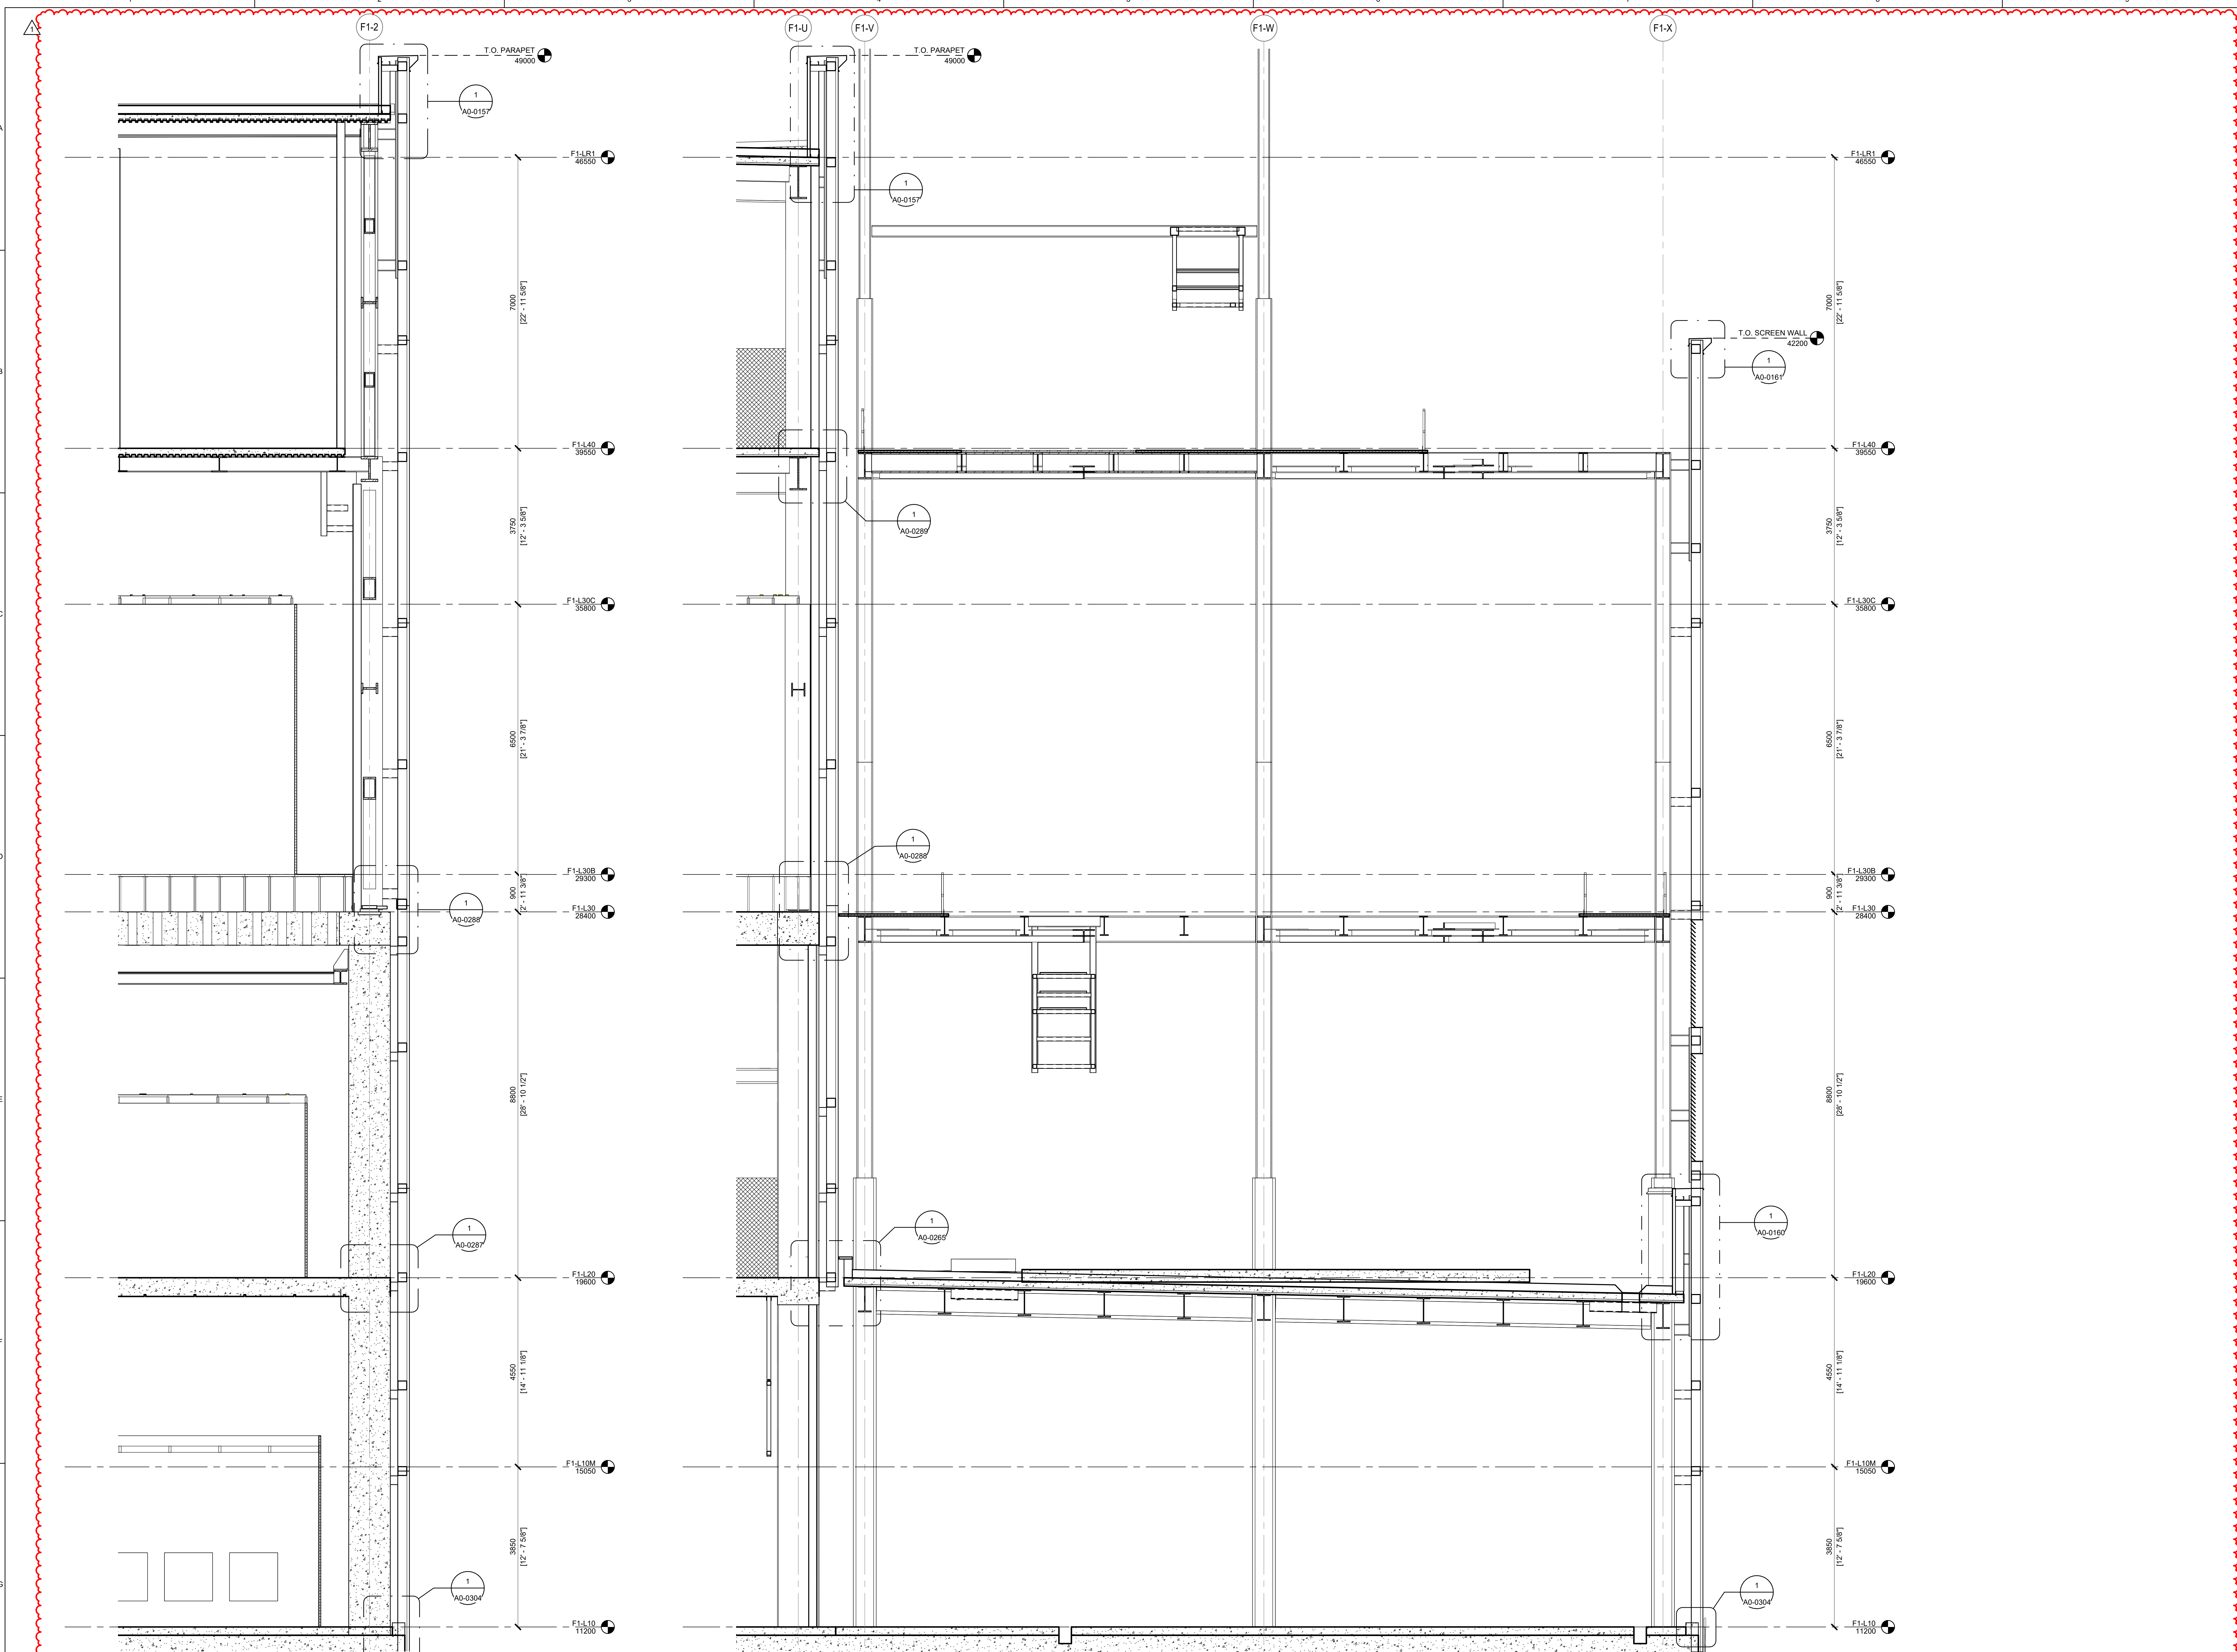

1 Section through West Facade @ F1-L&F1-M
1:50

2 Section through SUS @ F1-3&F1-4
1:50

PRELIMINARY
- NOT FOR
CONSTRUCTION

NO.	DATE	ENGINEER	DRAWN	CHECK	SD	IS	APPROVED	VM
0	26/06/25		PF-2025	ISSUED FOR CONSTRUCTION				




TATA SEMICONDUCTOR MANUFACTURING PRIVATE LIMITED
B-107, PH-10, TSI, AMBEGAON
Karna Bridge Old Hospital Road
AMBEGAON - 400160 (PUNE)



Jacobs Solutions India Private Limited
PLATINUM TOWER, PLOT NO. 184, MIDC VILHAR
PHASE-1, GURGAON - 122 006 (HARYANA), INDIA
TEL: +91-124-3317000 FAX: +91-124-3317299
www.Jacobs.com

Project Title:	DF1 DHOLERA SITE PHASE 1
Drawing Title:	FAB BUILDING 1 ARCHITECTURAL WALL SECTIONS
Date:	26/06/2025
Scale:	1:50
Proj. No.:	03898800
Drawing No.:	FB1A0-7305

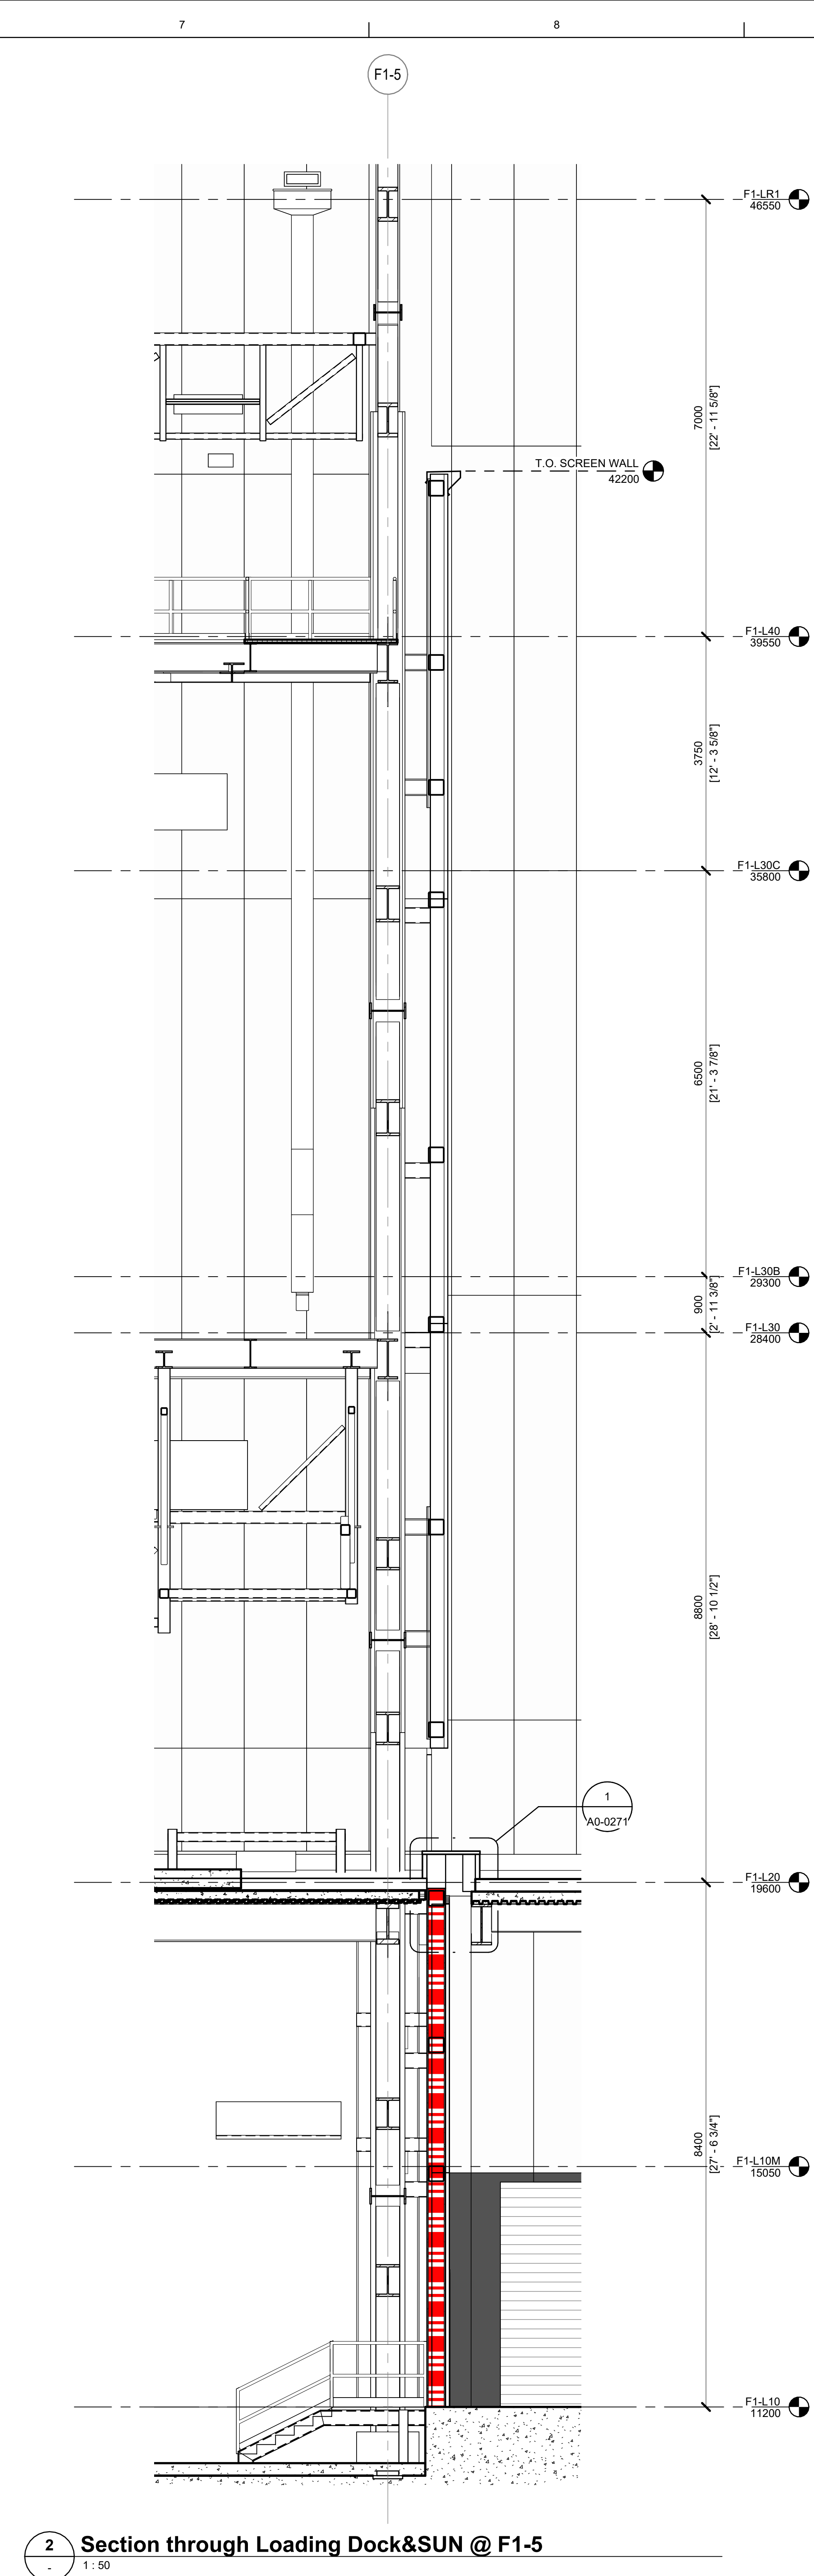

FB1A0-7306